

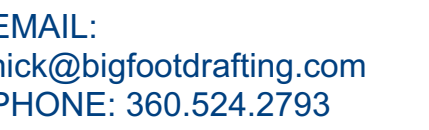


1. THIS DRAWING CONTAINS INFORMATION WHICH IS THE PROPERTY OF BIGFOOT DRAFTING LLC. THIS DRAWING IS RECEIVED IN CONFIDENCE AND ITS CONTENTS MAY NOT BE DISCLOSED WITHOUT PRIOR WRITTEN CONSENT OF BIGFOOT DRAFTING LLC. ORIGINAL PROJECT OWNER MAY MAKE AS MANY COPIES AS NEEDED FOR THE CONSTRUCTION OF THE ONE INTENDED PROJECT.
2. CONTRACTOR MUST VERIFY ALL DIMENSIONS, NOTES, AND DESIGN CRITERIA BEFORE THE START OF CONSTRUCTION AND WILL BE RESPONSIBLE FOR ALL ERRORS AND/OR OMISSIONS.
3. CONTRACTOR WILL BE RESPONSIBLE TO ADAPT THESE PLANS TO SUIT THE NEEDS OF THE BUILDING ON SITE, AS REQUIRED, PROVIDED SUCH ADJUSTMENTS DO NOT VIOLATE CODE, OR ALTER THE STRUCTURAL INTEGRITY OF THE BUILDING.
4. CONTRACTOR TO BE RESPONSIBLE FOR VENTILATION, WATER PROOFING, WATER FLASHING, CONSTRUCTION MEANS, METHODS, TECHNIQUES, PRECAUTIONS AND PROGRAMS IN CONNECTION WITH THE WORK.
5. THESE DRAWINGS HAVE BEEN PREPARED FOR REFERENCE OF ELECTRICAL, MECHANICAL, AND OTHER BUILDING SYSTEMS IF REQUIRED TO BE DONE BY OTHERS.
6. IF THE CONTRACTOR DISCOVERS ANY DEFECTS IN THE CONSTRUCTION DOCUMENTS, HE SHALL PROVIDE WRITTEN NOTICE OF THAT DEFECT TO BIGFOOT DRAFTING AND ALLOW ENOUGH TIME TO CORRECT THE DEFECT. IF THE CONTRACTOR FAILS TO DO SO, THEY SHALL BEAR ALL COSTS ASSOCIATED WITH SAID DEFECT.

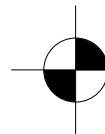

DESIGN CRITERIA	
FLOOR LOAD	40# LL 12# DL
DECK LOAD	60# LL 10# DL
ROOF SNOW	25# LL 17# DL
GROUND SNOW	30#
FROST DEPTH	12"
EXPOSURE CAT	B

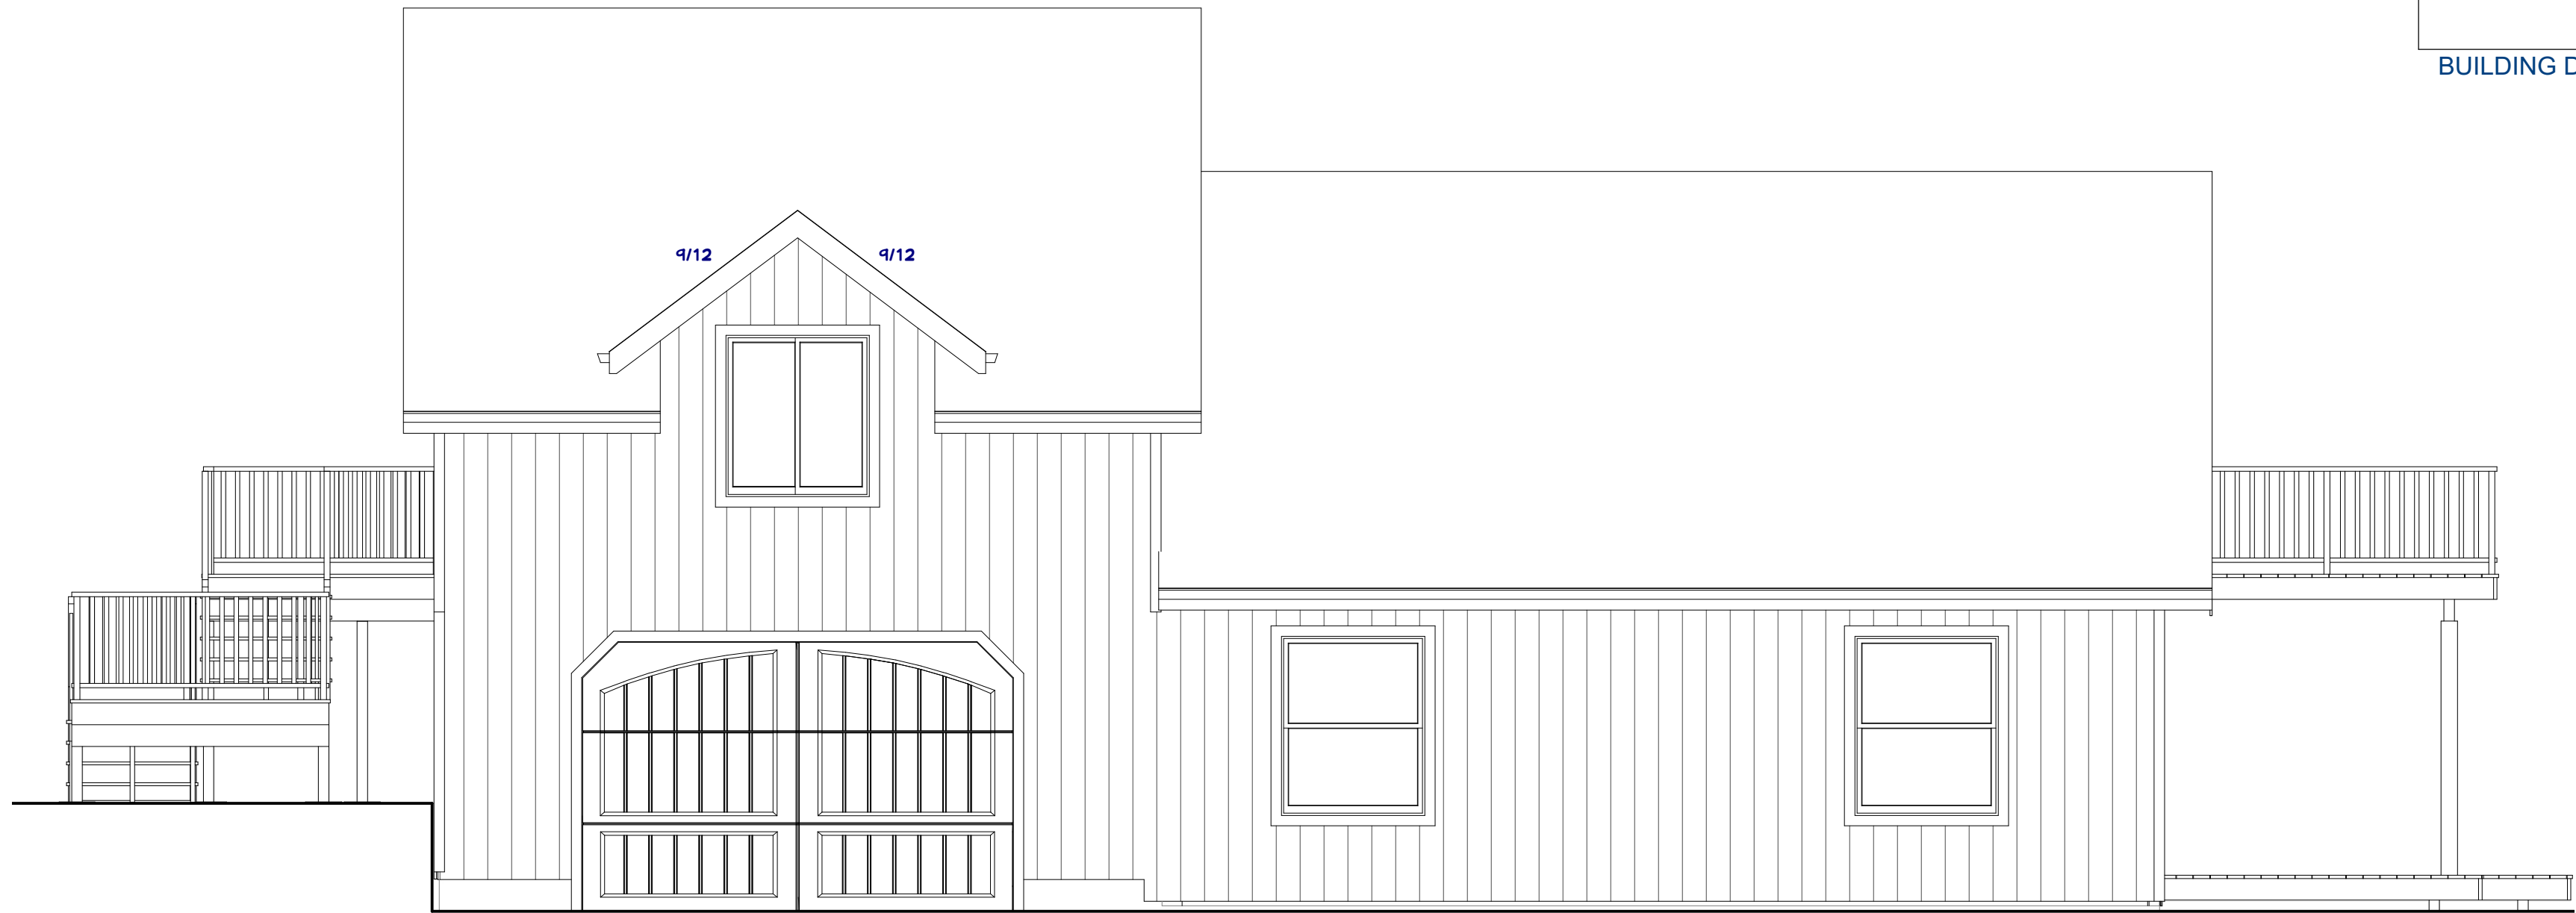


EX

REVISION TABLE	DATE	REVISED BY
----------------	------	------------

9/18/2026

1

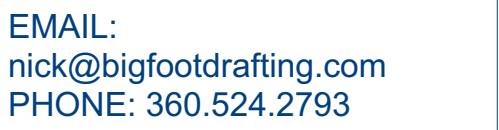

BUILDING DEPARTMENT STAMP

DESIGN CRITERIA	
FLOOR LOAD	40# LL 12# DL
DECK LOAD	60# LL 10# DL
ROOF SNOW	25# LL 17# DL
GROUND SNOW	30#
FROST DEPTH	12"
EXPOSURE CAT	B

PROJECT NAME
ELEVATIONS

[illegible]

DATE:

9/18/2026

SHEET:

2





BUILDING DEPARTMENT STAMP

DESIGN CRITERIA	
FLOOR LOAD	40# LL 12# DL
DECK LOAD	60# LL 10# DL
ROOF SNOW	25# LL 17# DL
GROUND SNOW	30#
FROST DEPTH	12"
EXPOSURE CAT	B


PROJECT NAME

[illegible]

DATE:


9/18/2026

SHEET

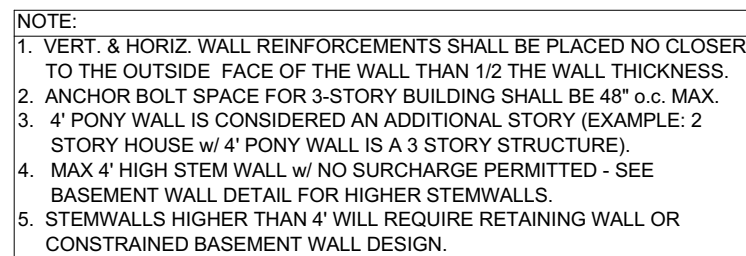


4'-0" MAX. FOUNDATION w/ SLAB
SCALE: 1/2"=1'


1 FOUND UNDER 4' W/ SLAB
1/2 IN = 1 FT

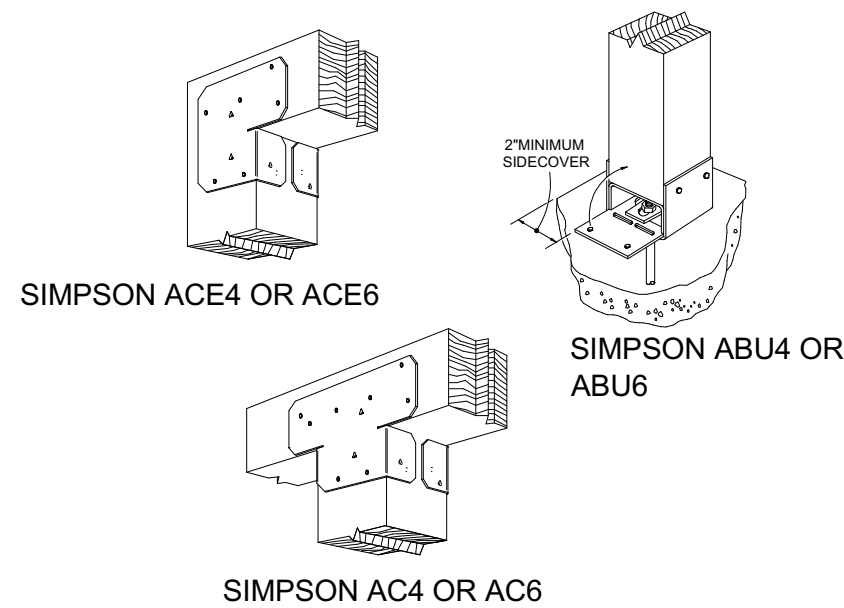

 POST CONNECTIONS
1 1/2 IN = 1 FT

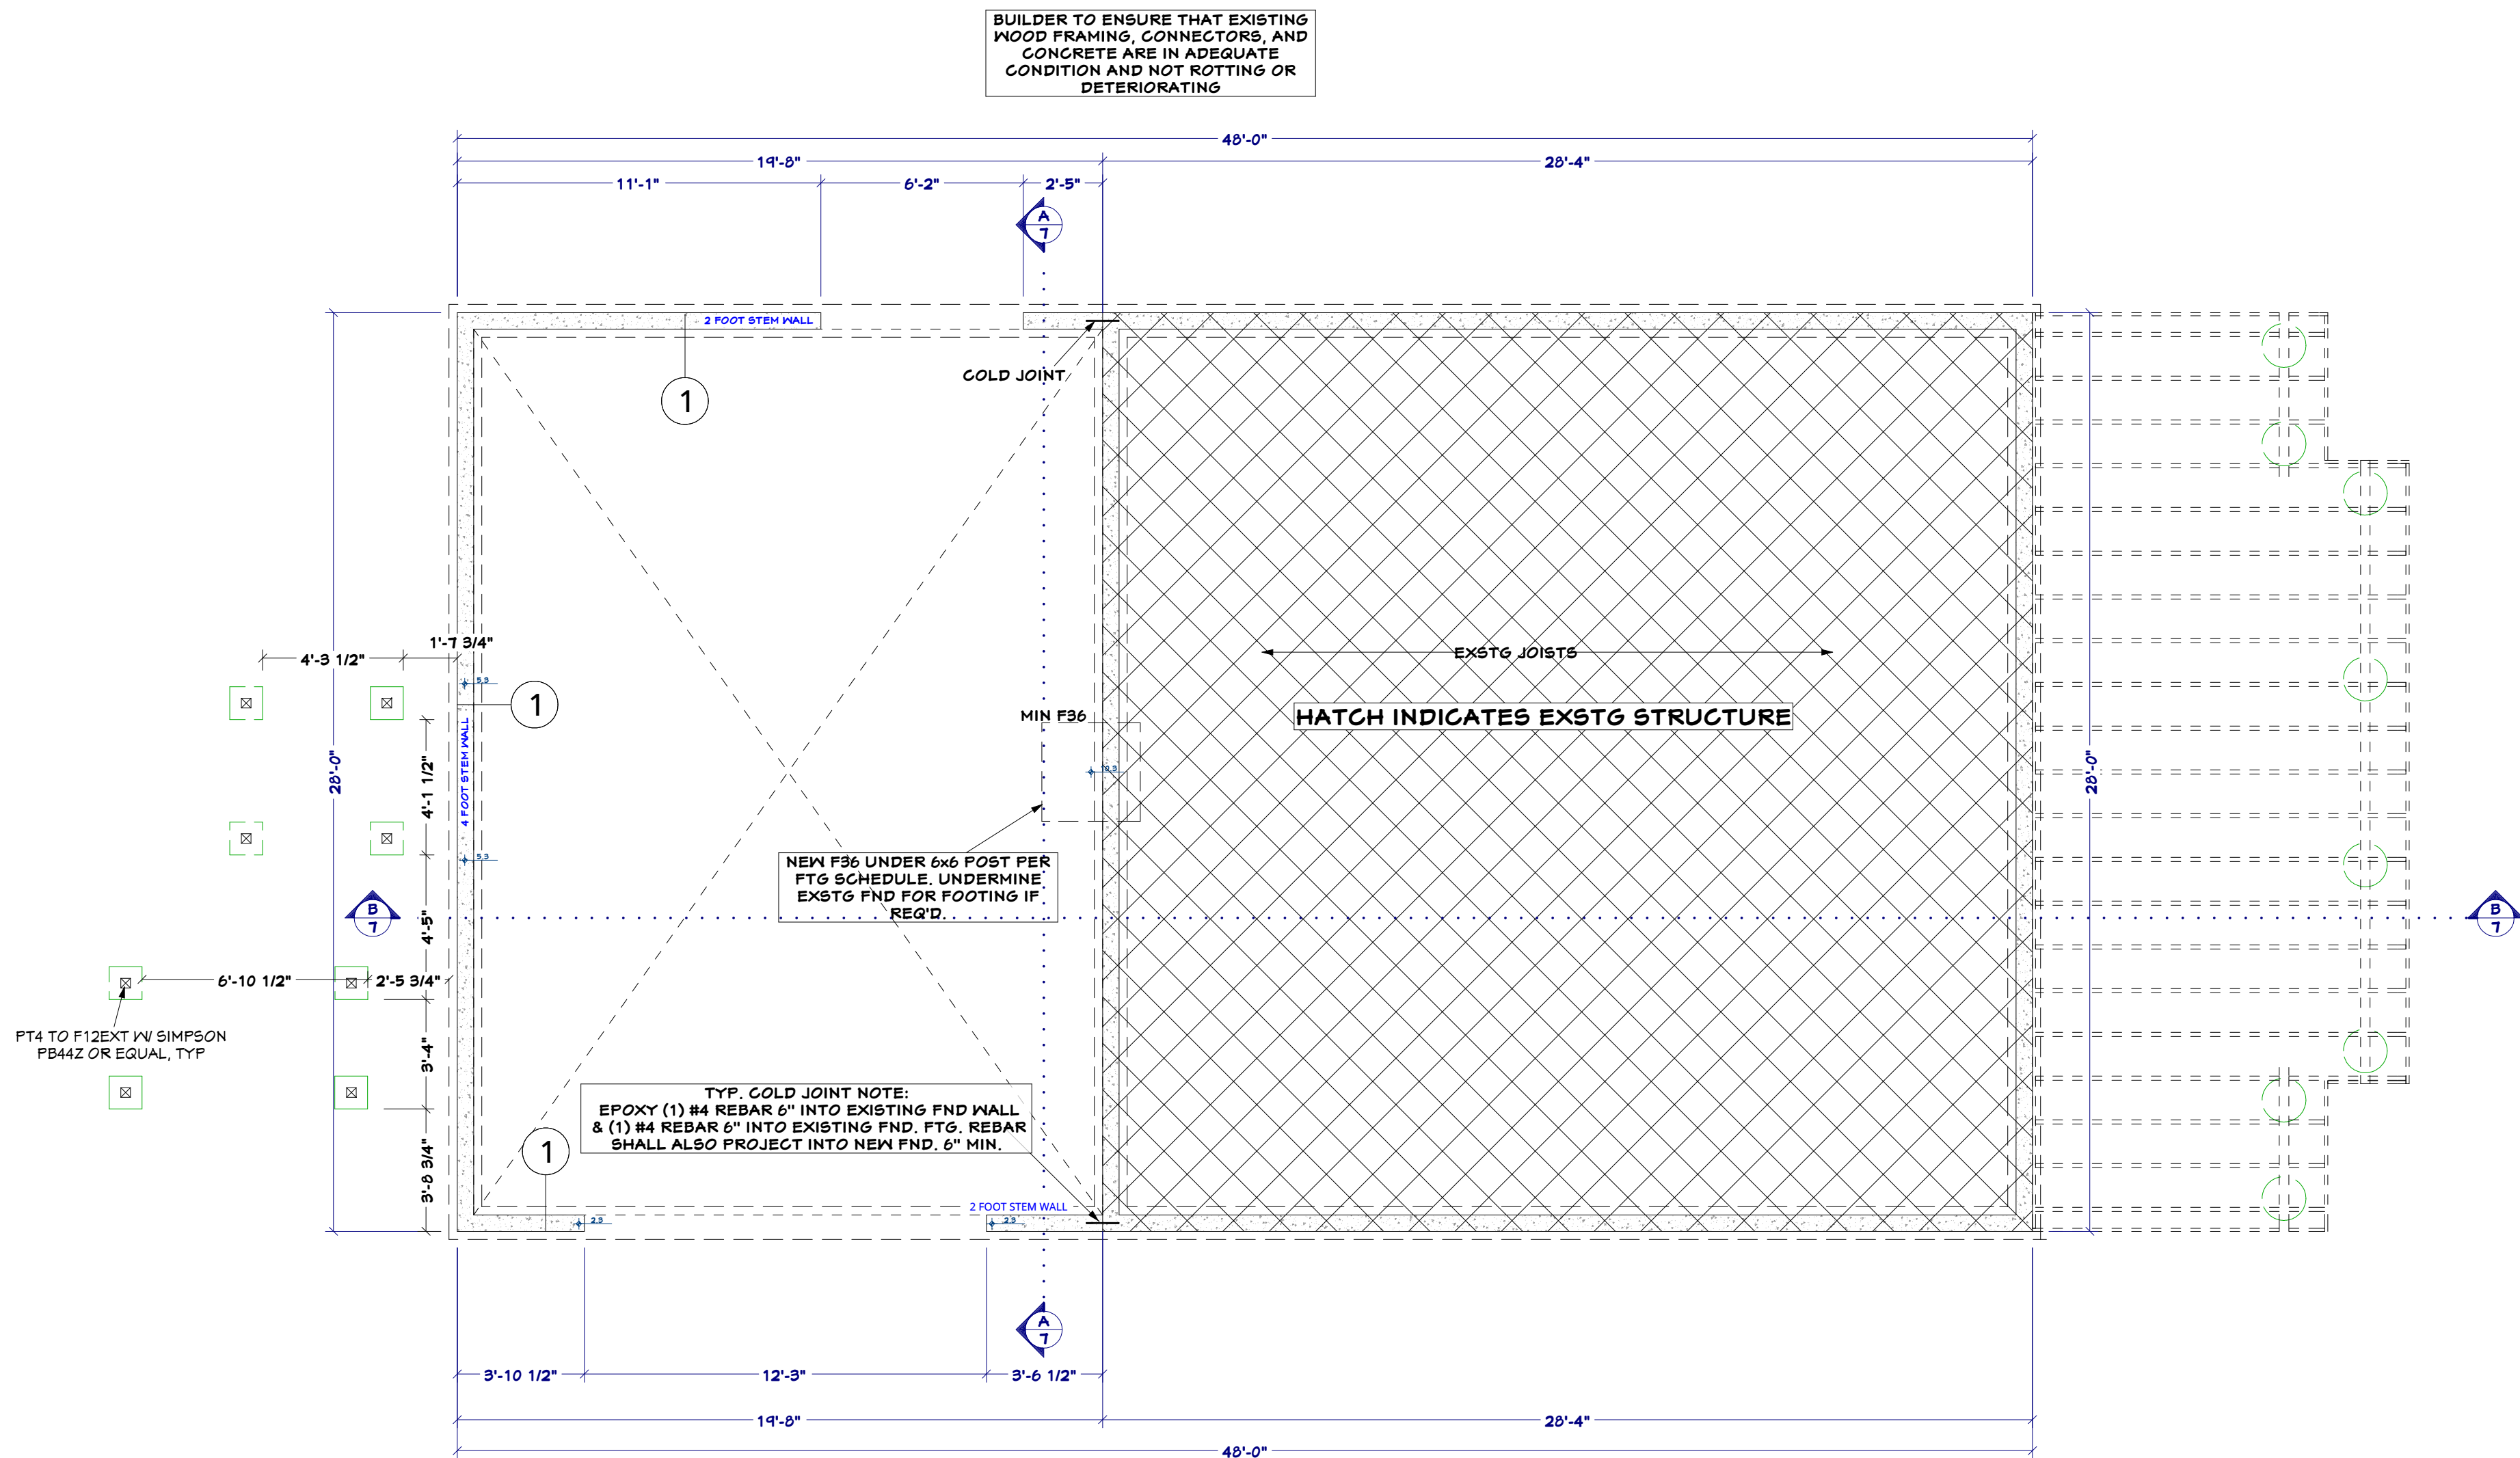

 FOUNDATION
1/4 IN = 1 FT

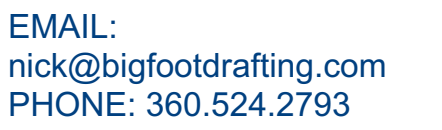

DESIGN CRITERIA	
FLOOR LOAD	40# LL 12# DL
DECK LOAD	60# LL 10# DL
ROOF SNOW	25# LL 17# DL
GROUND SNOW	30#
FROST DEPTH	12"
EXPOSURE CAT	B

PROJECT NAME

[illegible]

9/18/2026


SHEET:

NOTES:


1. BRACE PANELS
2. G-595-96 CONTINUOUSLY SHEATHED WOOD STRUCTURAL PANEL 3/8" MIN. SHEATHING FASTENED USING 8D NAILS SPACED @ 6" O.C. EDGES AND 12" O.C. FIELD.
3. SHEETROCK - 1/2" SIDED GYPSUM BOARD STRUCTURAL PANEL 12" MIN. SHEETROCK FASTENED USING 5D COOLER NAILS SPACED @ 7" O.C. EDGE AND 7" O.C. FIELD.
4. FLASHING - 1/2" MOIST DIRECTLY UNDER PARALLEL BRACE WALLS. SEE DETAIL 18 SHEET A-501.
5. BLOCK BETWEEN ROOST RUNNING PERPENDICULAR TO BRACE PANELS. SEE DETAIL 18 SHEET A-501.
6. SEE ATTACHED AFT MAINT BRACING REPORT FOR INDIVIDUAL WALL BRACING DETAILS.

EXISTING STRUCTURE IS
ADEQUATE TO RESIST ANY
ADDITIONAL LATERAL LOADS
CREATED FROM NEW ADDITION.

**BUILDER TO ENSURE THAT EXISTING
WOOD FRAMING, CONNECTORS, AND
CONCRETE ARE IN ADEQUATE
CONDITION AND NOT ROTTING OR
DETERIORATING**

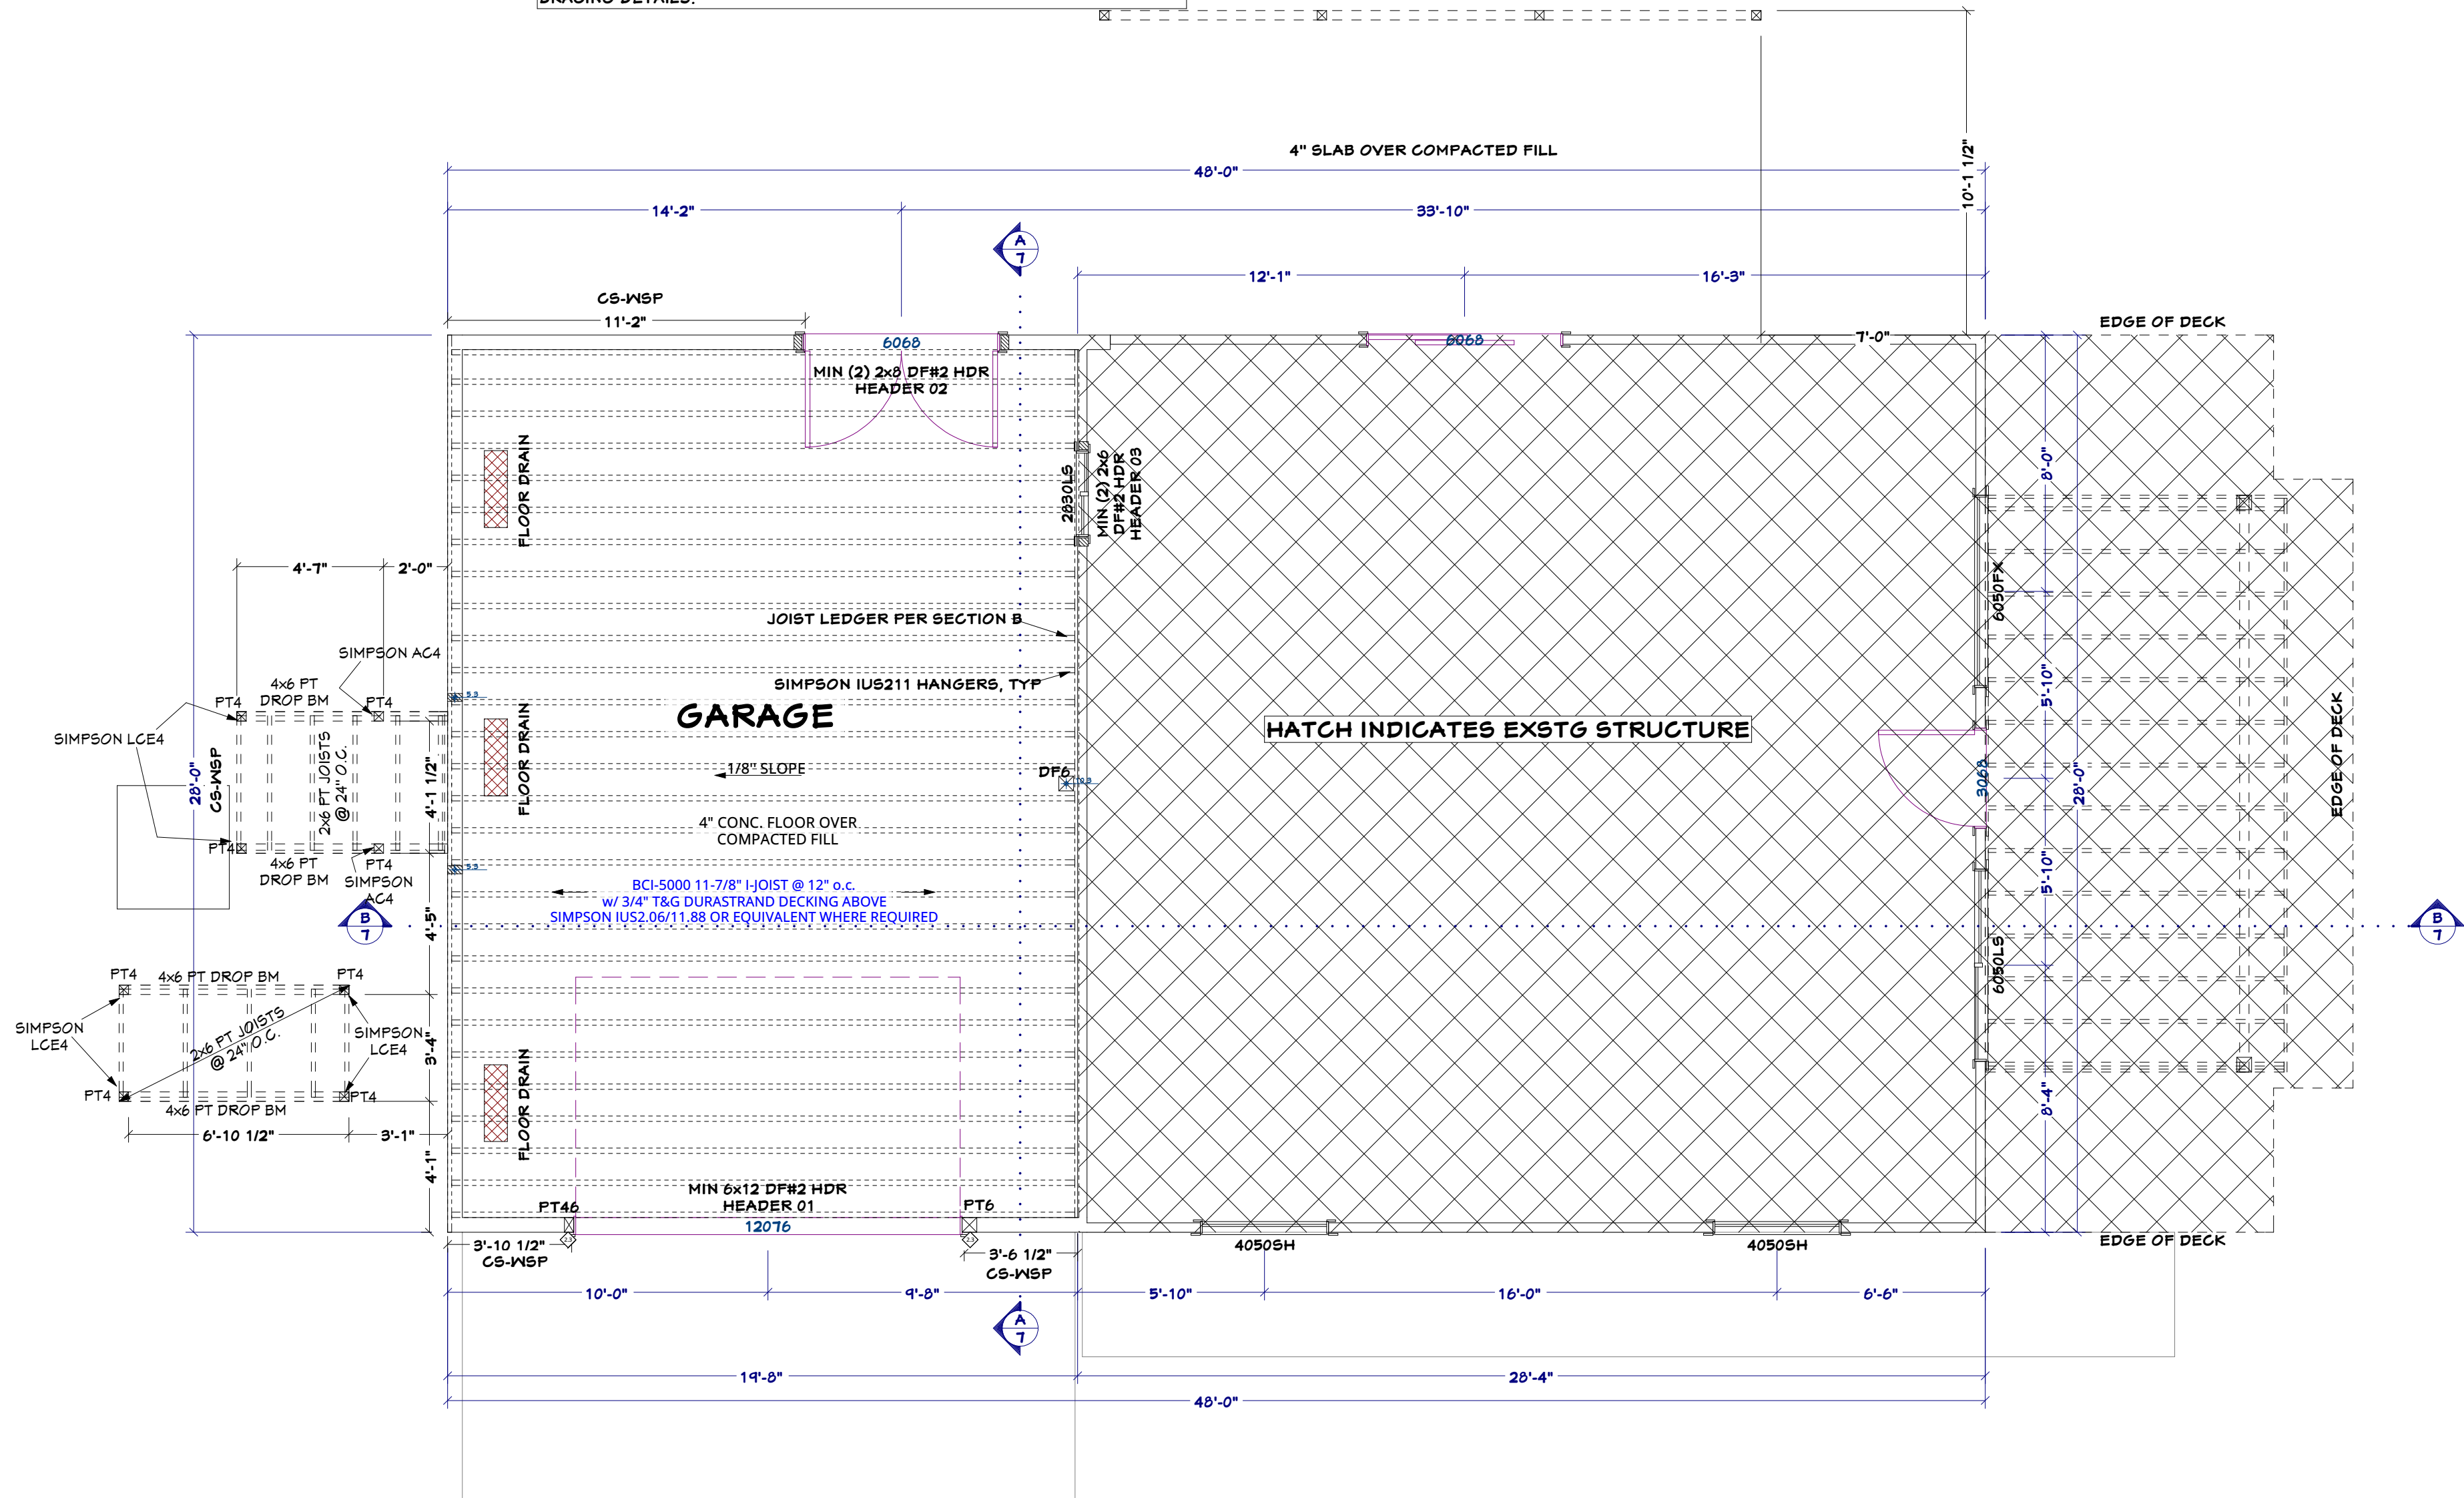

1ST FLOOR
1/4 IN = 1 FT

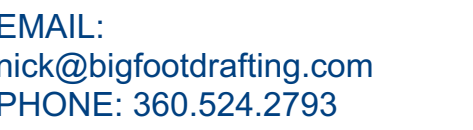

BUILDING DEPARTMENT STAMP

DESIGN CRITERIA		
FLOOR LOAD	40# LL 12# DL	
DECK LOAD	60# LL 10# DL	
ROOF SNOW	25# LL 17# DL	
GROUND SNOW	30#	
FROST DEPTH	12"	
EXPOSURE CAT	B	

PROJECT NAME

[illegible]

DATE:


9/18/2026

SHEET:


1. BRACE PANELS
 - A. GS-WSP - CONTINUOUSLY SHEATHED WOOD STRUCTURAL PANEL 3/8" MIN. SHEETING FASTENED USING 5D NAILS SPACE @ 4" O.C. EDGES AND 12" O.C. FIELD.
 - B. GB-25-4FT - 2 SIDED GYPSUM BOARD STRUCTURAL PANEL 1/2" SHEETROCK FASTENED USING 5D COOLER NAILS SPACED @ 1" O.C. EDGE AND 12" O.C. FIELD.
2. PLACE 1 FLOOR JOIST DIRECTLY UNDER PARALLEL BRACE PANELS. SEE DETAIL 20 SHEET A-501.
3. BLOCK BETWEEN JOIST RUNNING PERPENDICULAR TO BRACE PANELS. SEE DETAIL 49 SHEET A-501.
4. SEE ATTACHED AFA WALL BRACING REPORT FOR INDIVIDUAL WALL BRACING DETAILS.

EXISTING STRUCTURE IS
ADEQUATE TO RESIST ANY
ADDITIONAL LATERAL LOADS
CREATED FROM NEW ADDITION.

**BUILDER TO ENSURE THAT EXISTING
WOOD FRAMING, CONNECTORS, AND
CONCRETE ARE IN ADEQUATE
CONDITION AND NOT ROTTING OR
DETERIORATING**

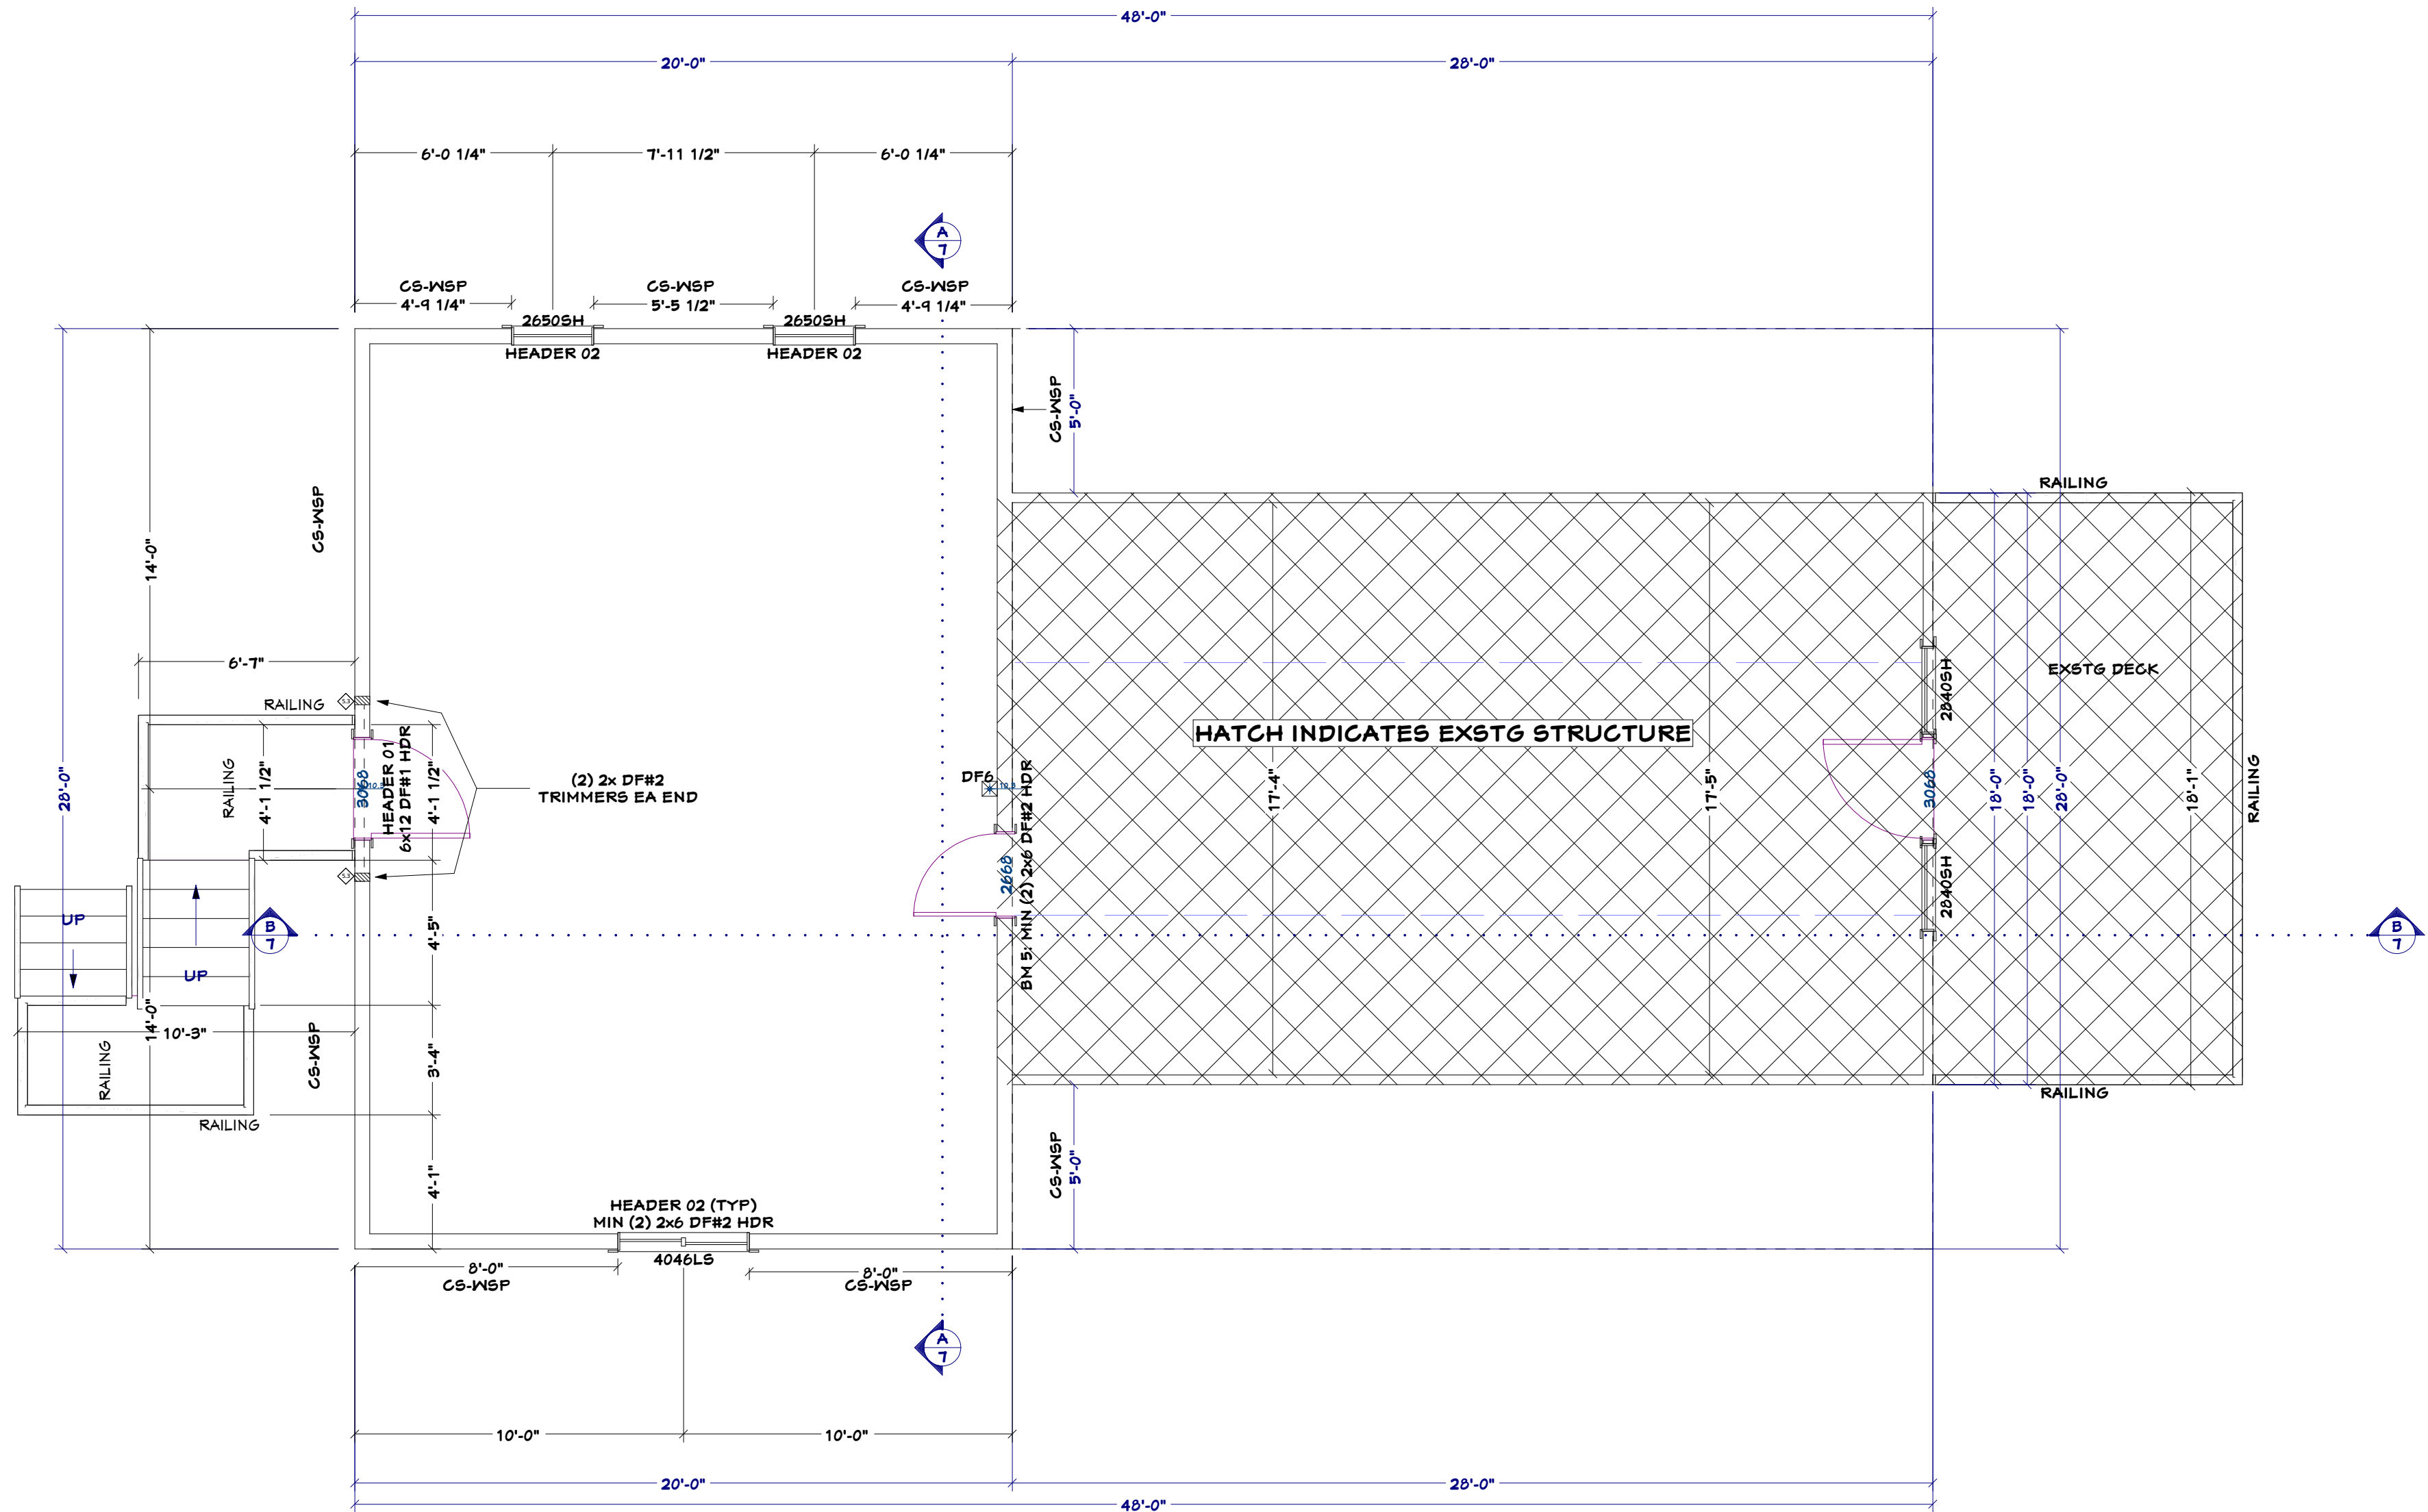

2ND FLOOR
1/4 IN = 1 FT

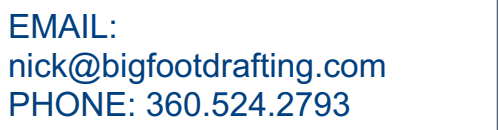

BUILDING DEPARTMENT STAMP

DESIGN CRITERIA	
FLOOR LOAD	40# LL 12# DL
DECK LOAD	60# LL 10# DL
ROOF SNOW	25# LL 17# DL
GROUND SNOW	30#
FROST DEPTH	12"
EXPOSURE CAT	B


PROJECT NAME

[illegible]

DATE:

9/18/2026

SHEET:

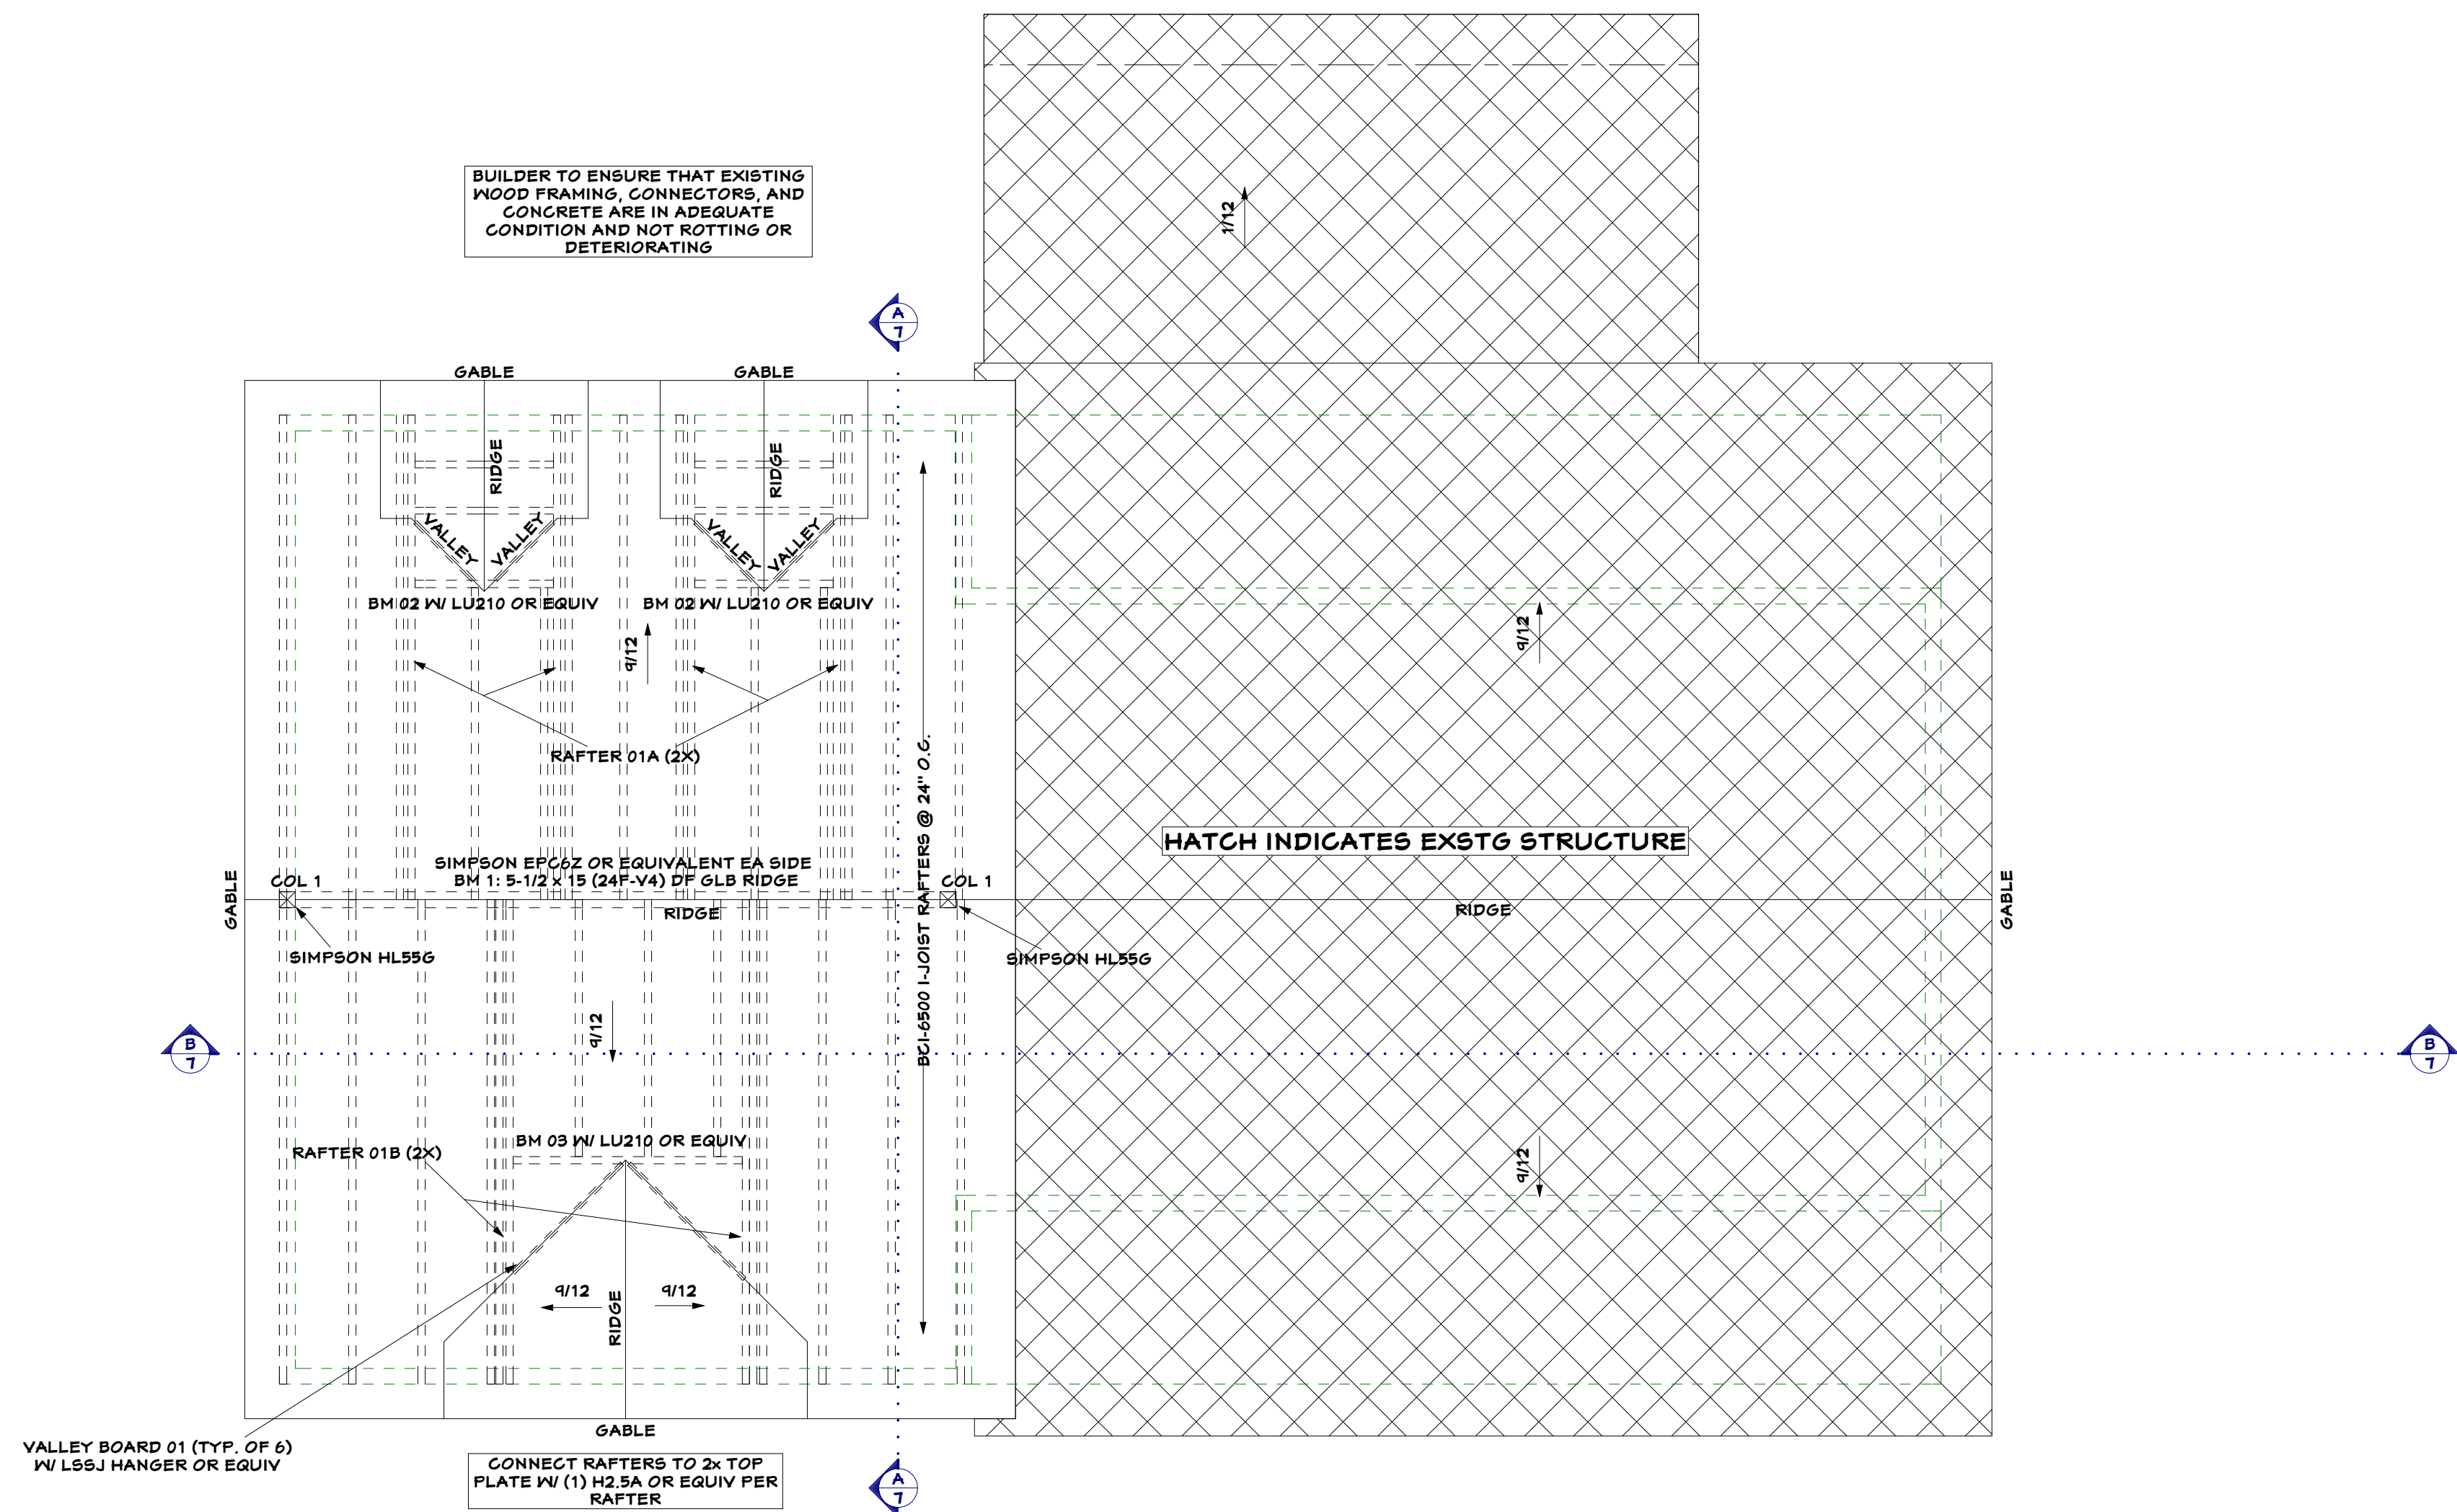

ROOF PLAN
1/4 IN = 1 FT



DESIGN CRITERIA	
FLOOR LOAD	40# LL 12# DL
DECK LOAD	60# LL 10# DL
ROOF SNOW	25# LL 17# DL
GROUND SNOW	30#
FROST DEPTH	12"
EXPOSURE CAT	B

